



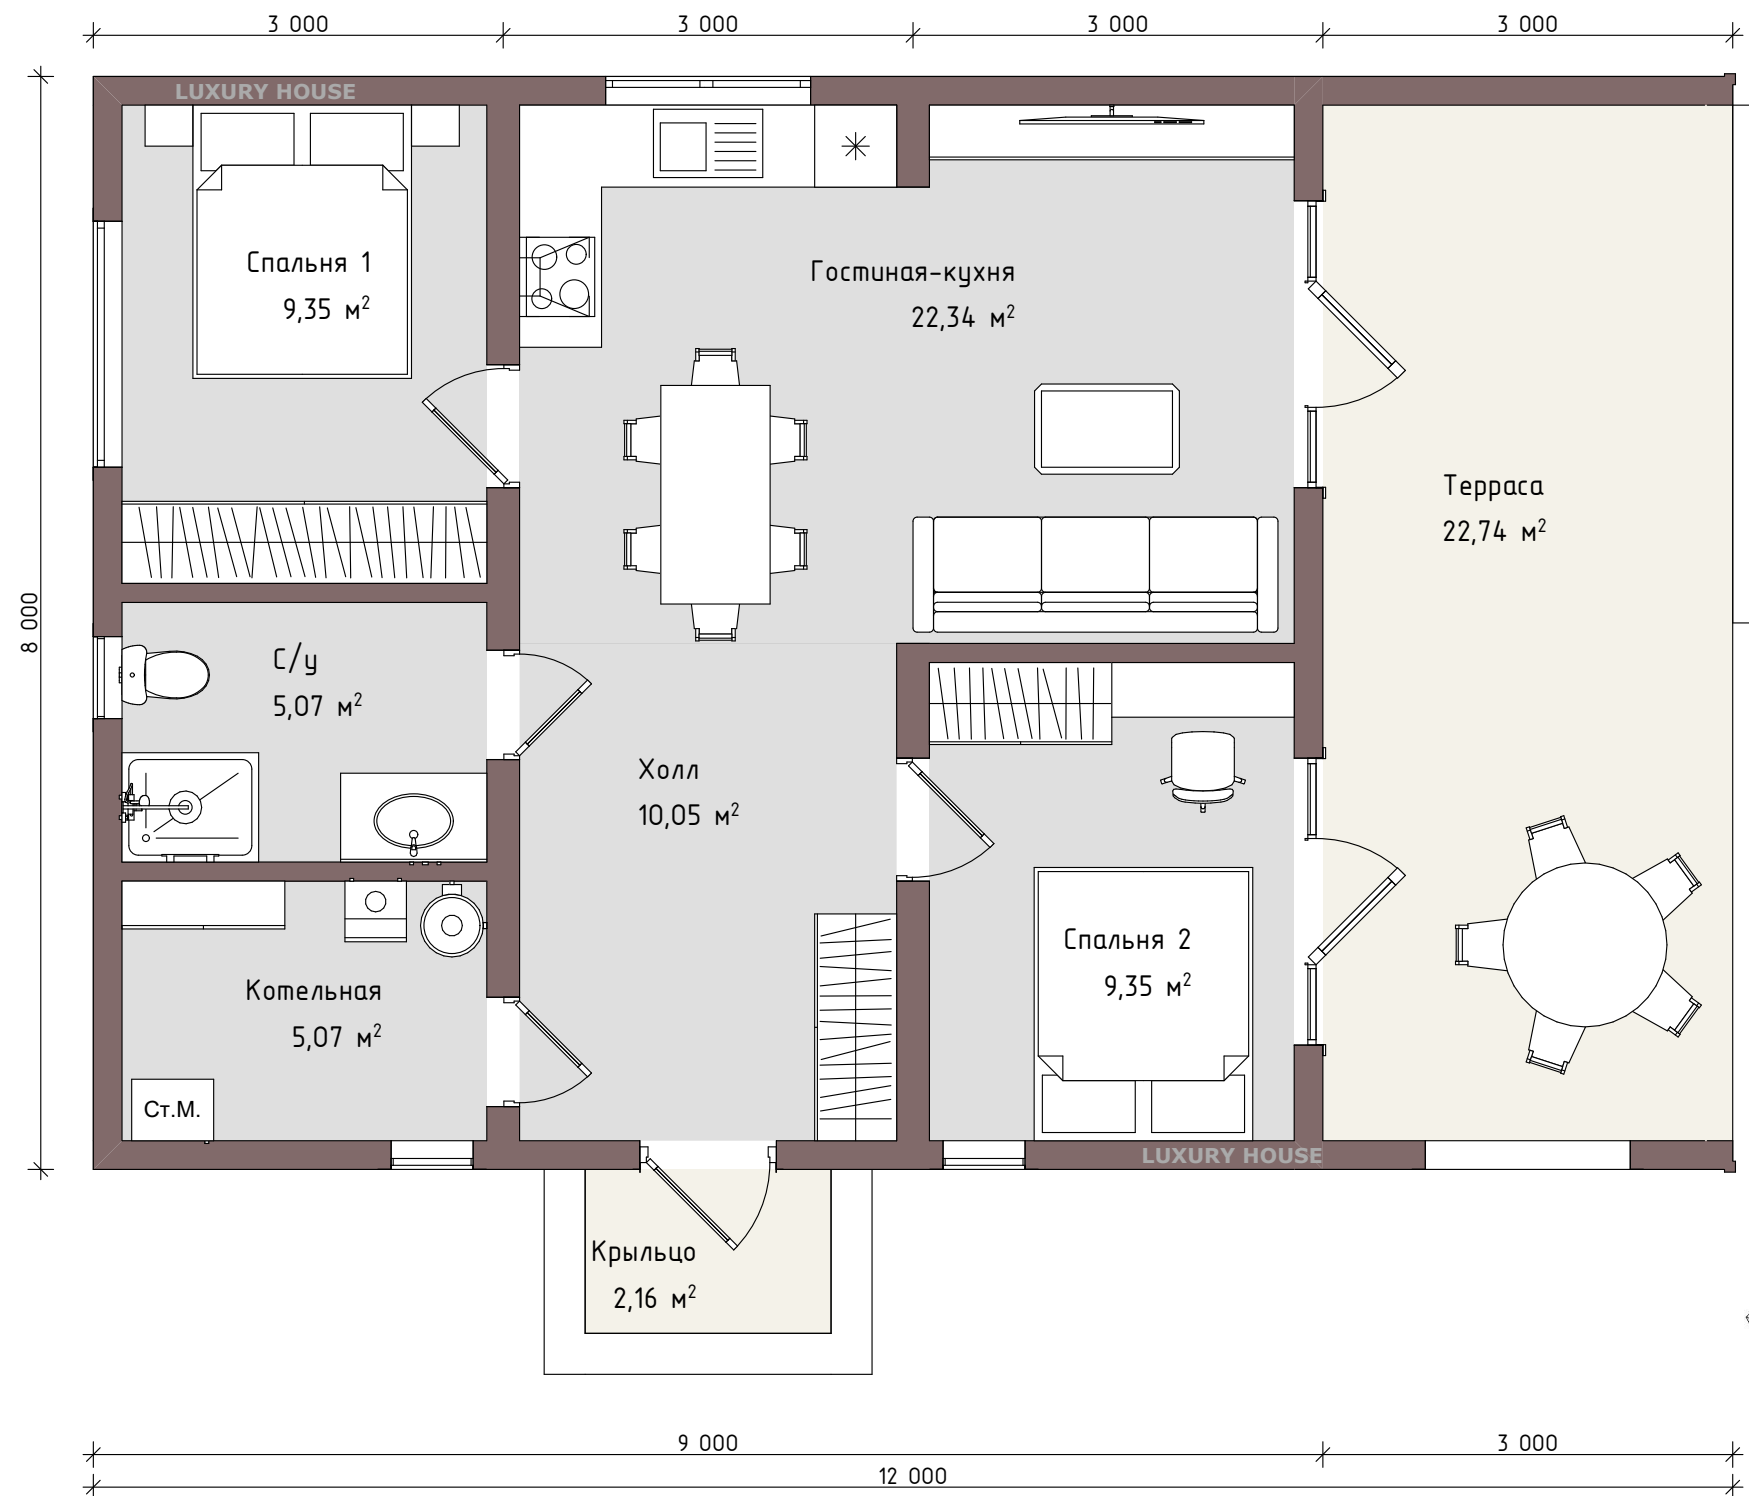


Экспликация помещений первого этажа		
№	Наименование	Площадь, м2
1	Холл	10,05
2	Котельная	5,07
3	С/у	5,07
4	Спальня 1	9,35
5	Гостиная-кухня	22,34
6	Спальня 2	9,35
7	Крыльцо	2,16
8	Терраса	22,74
		86,13 м²

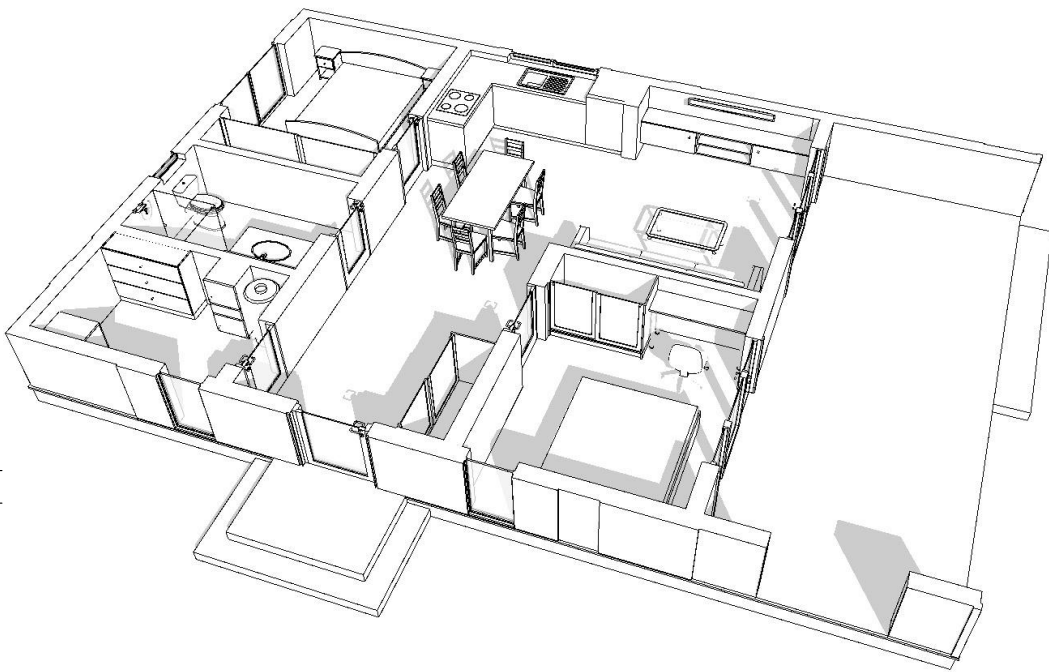

Примечание:

- 1. За отм. 0.000 принят уровень чистого пола 1-го этажа.
- 2. Расстановка мебели и оборудования носит рекомендательный характер.
- 3. Направление открывания дверных полотен носит рекомендательный характер.
- 4. Площади помещений указаны без учета толщины отделочных материалов

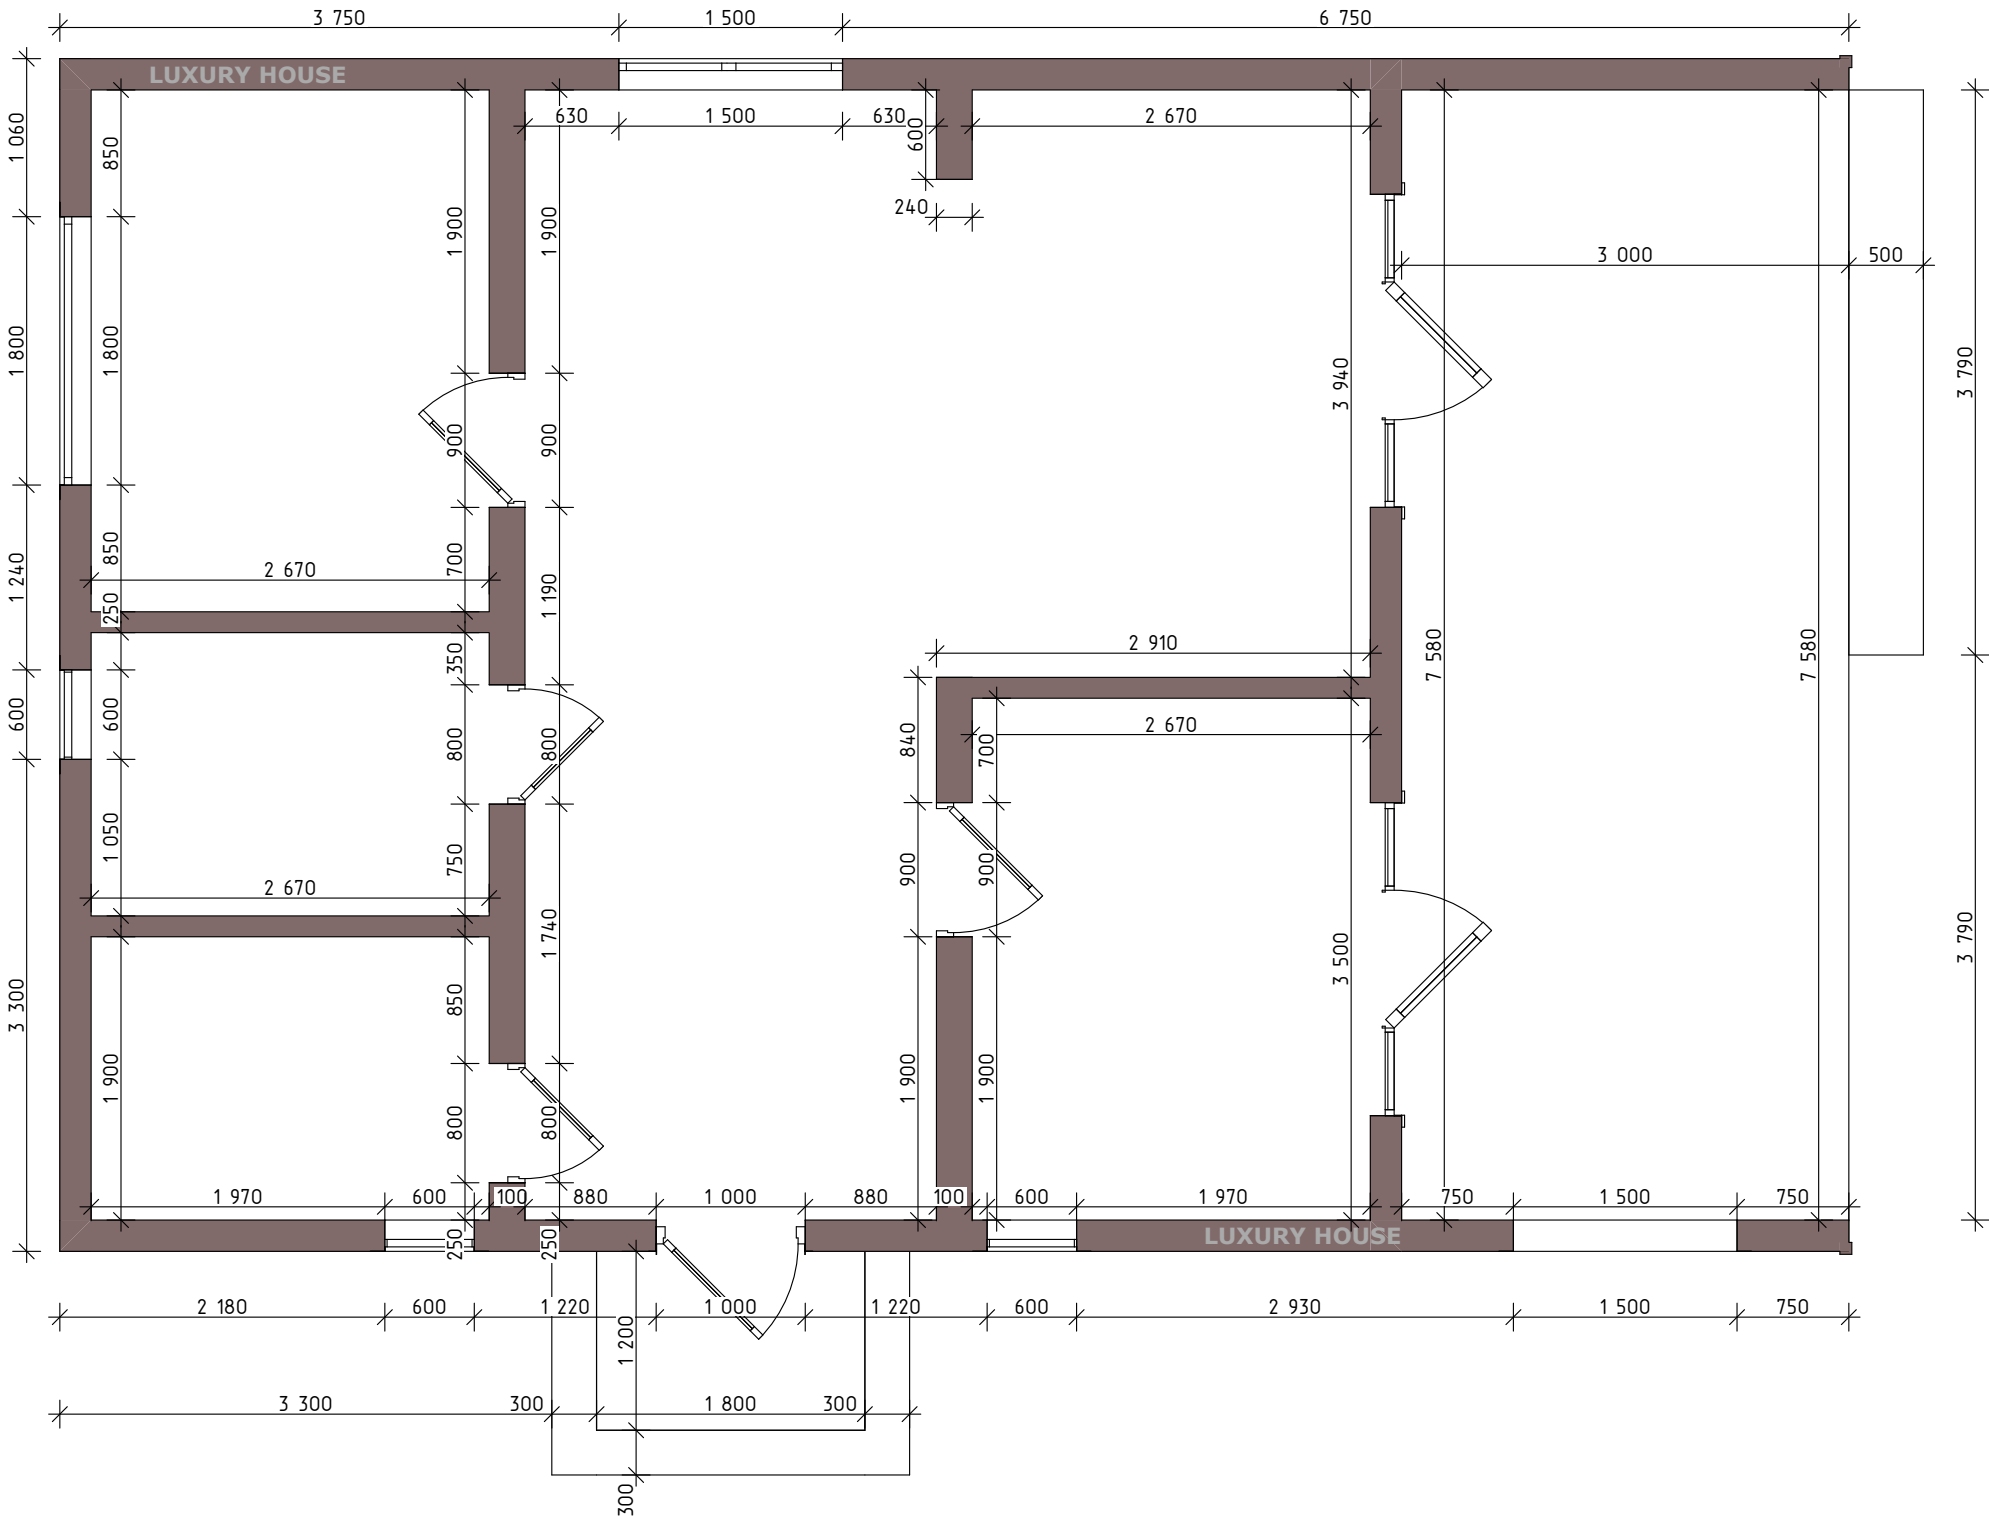

Экспликация помещений первого этажа		
№	Наименование	Площадь, м2
1	Холл	10,05
2	Котельная	5,07
3	С/у	5,07
4	Спальня 1	9,35
5	Гостиная-кухня	22,34
6	Спальня 2	9,35
7	Крыльцо	2,16
8	Терраса	22,74
		86,13 м²

Планировка

Фасад

Объемы материалов

LUXURY HOUSE



Планировка

Фасад

Объемы материалов



LUXURY HOUSE



Планировка

Фасад

Объемы материалов



LUXURY HOUSE